


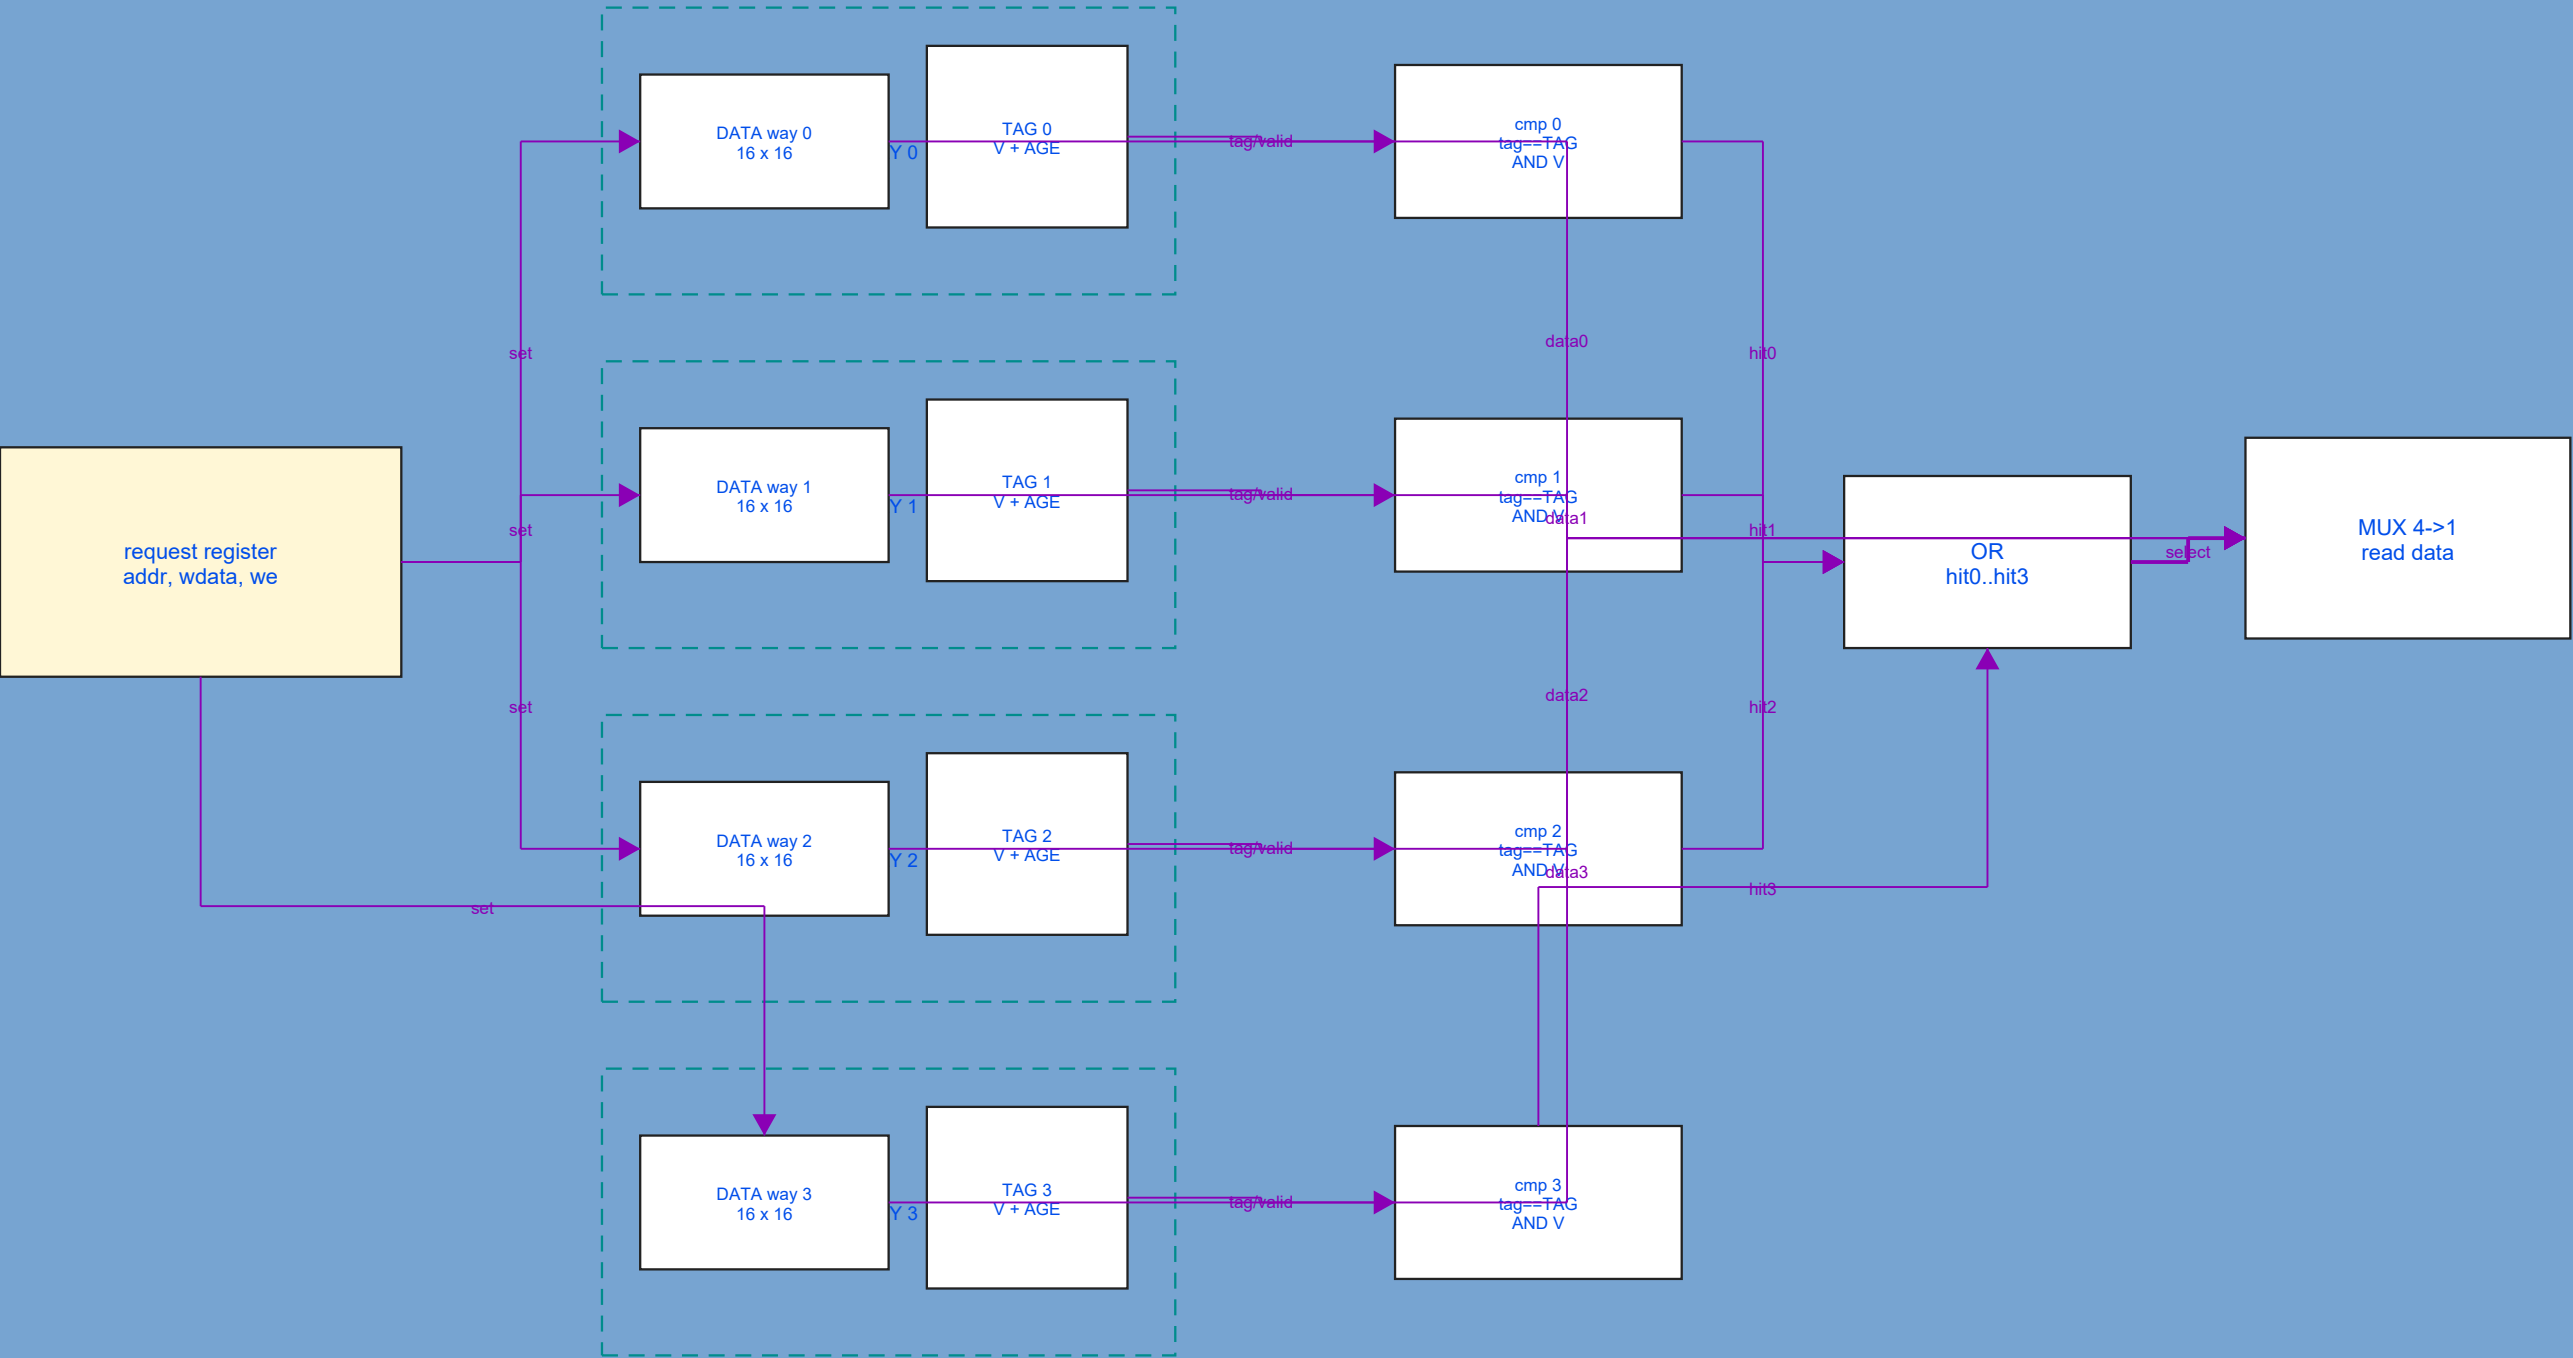

ПРИЛОЖЕНИЕ X
Блок данных кэша

Разраб.
Власов Р.Е.
Пров.
Третьяков

СифО ЭВМ
схема для
печати