


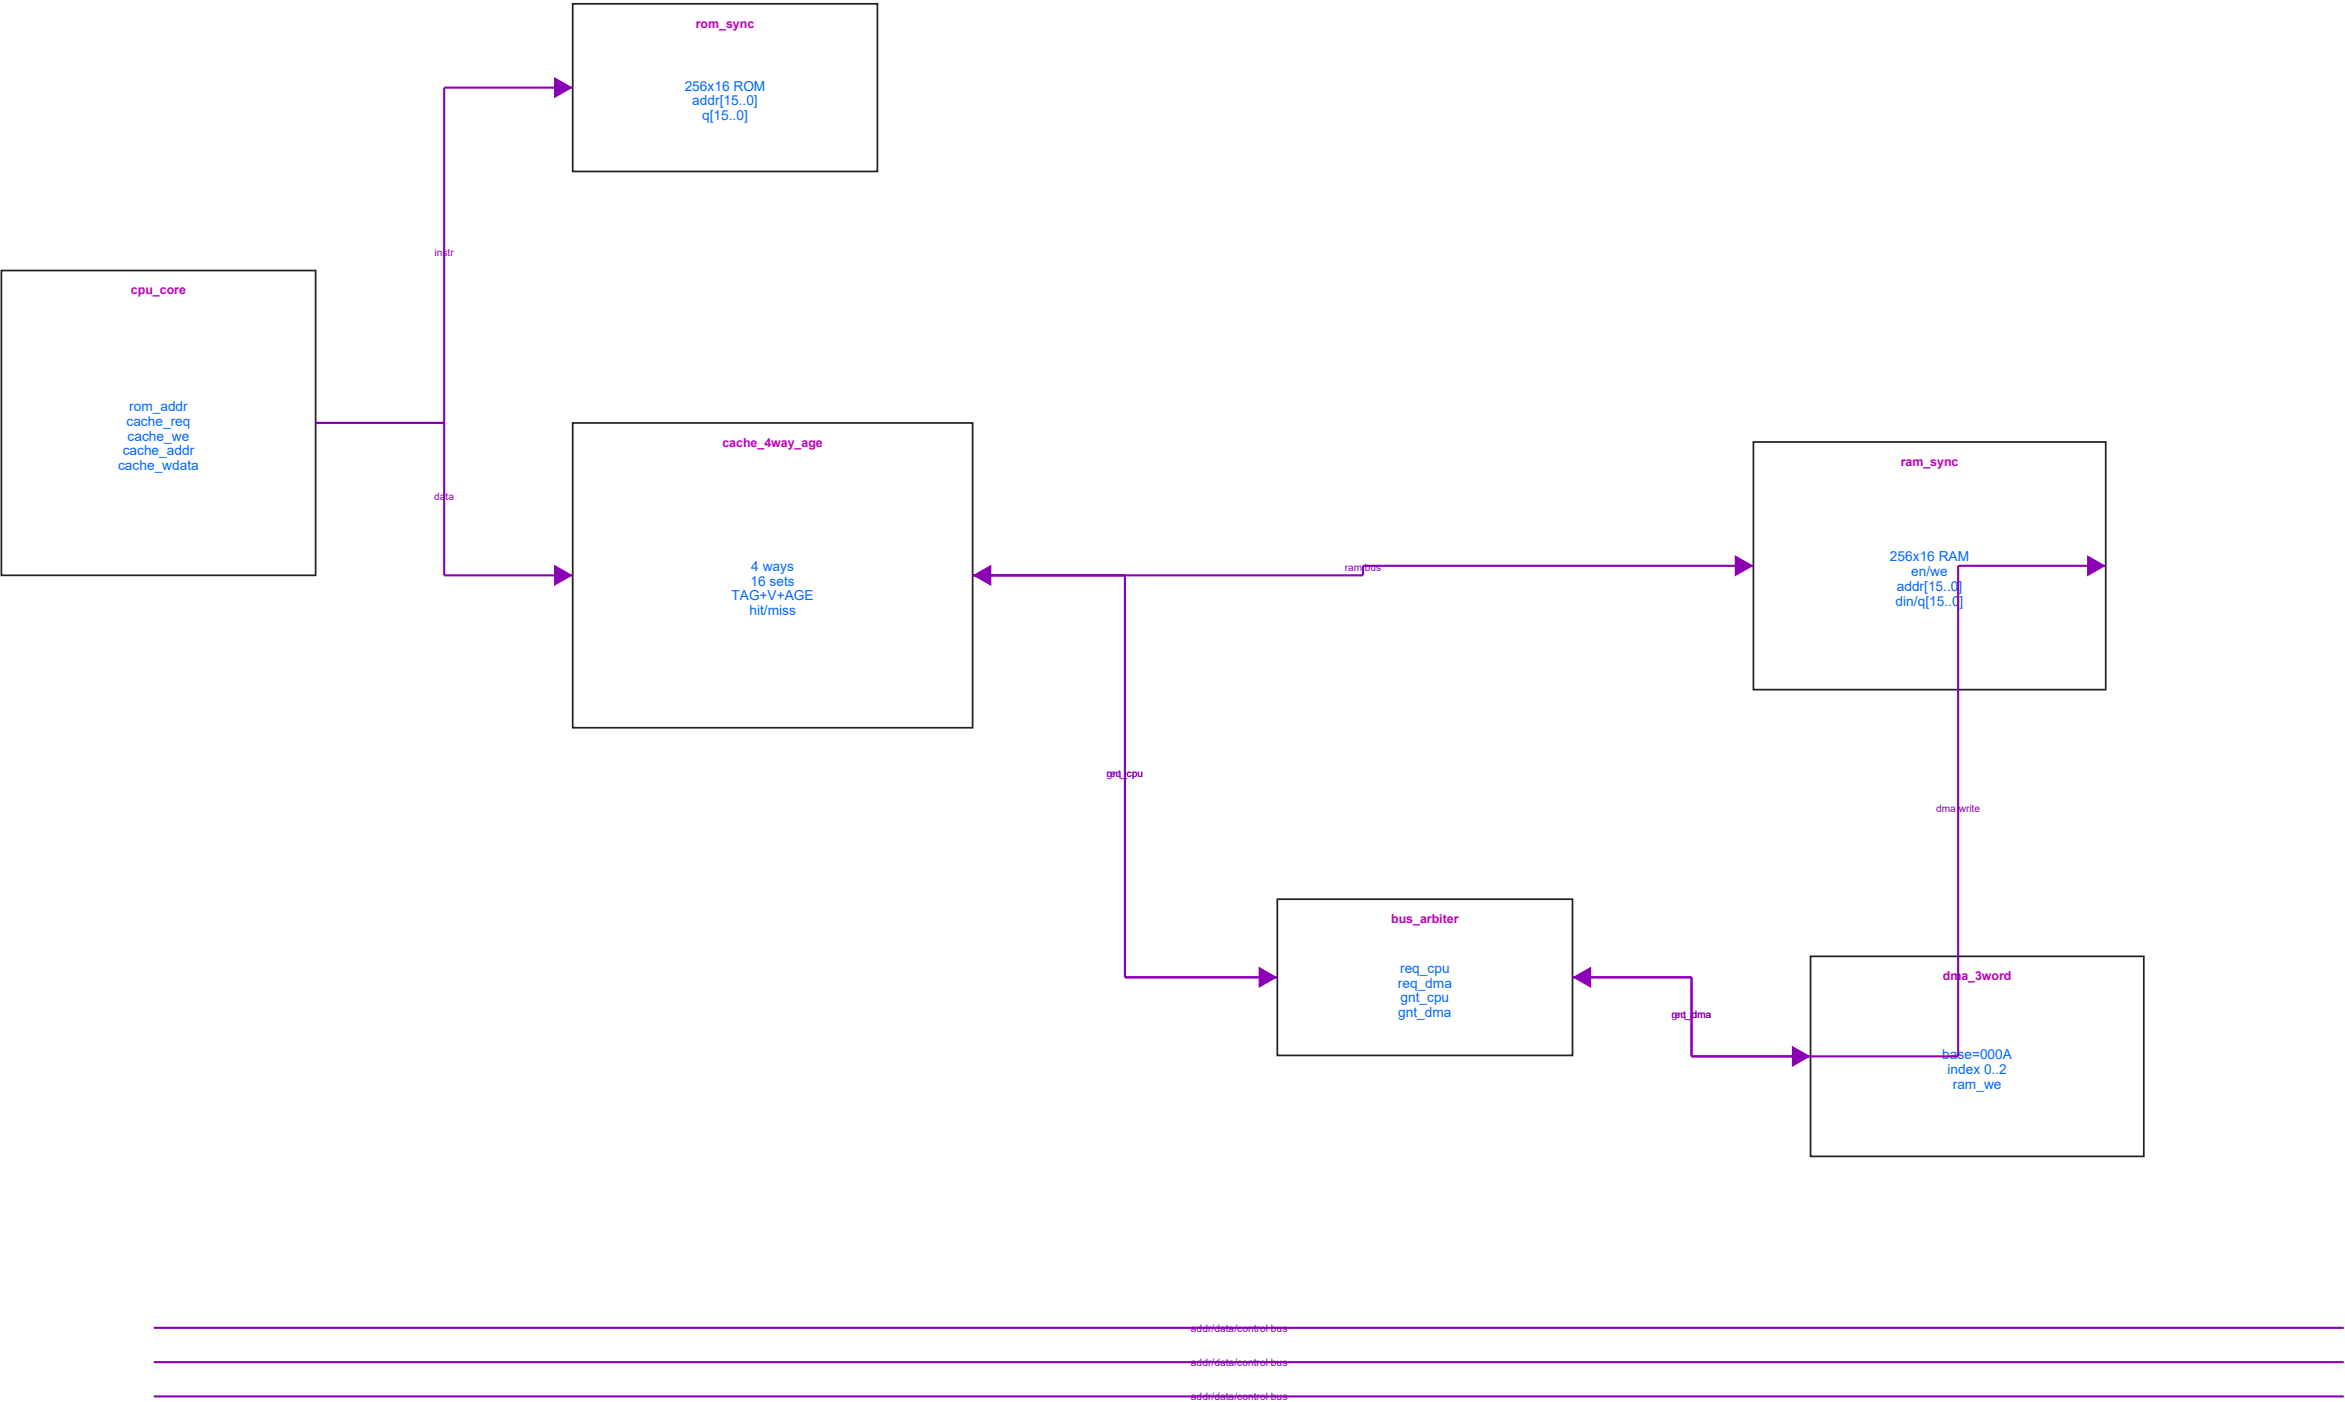

ПРИЛОЖЕНИЕ Б
Схема совмещенного блока ЗУ

Разраб. Власов Р.Е.
Пров. Третьяков