


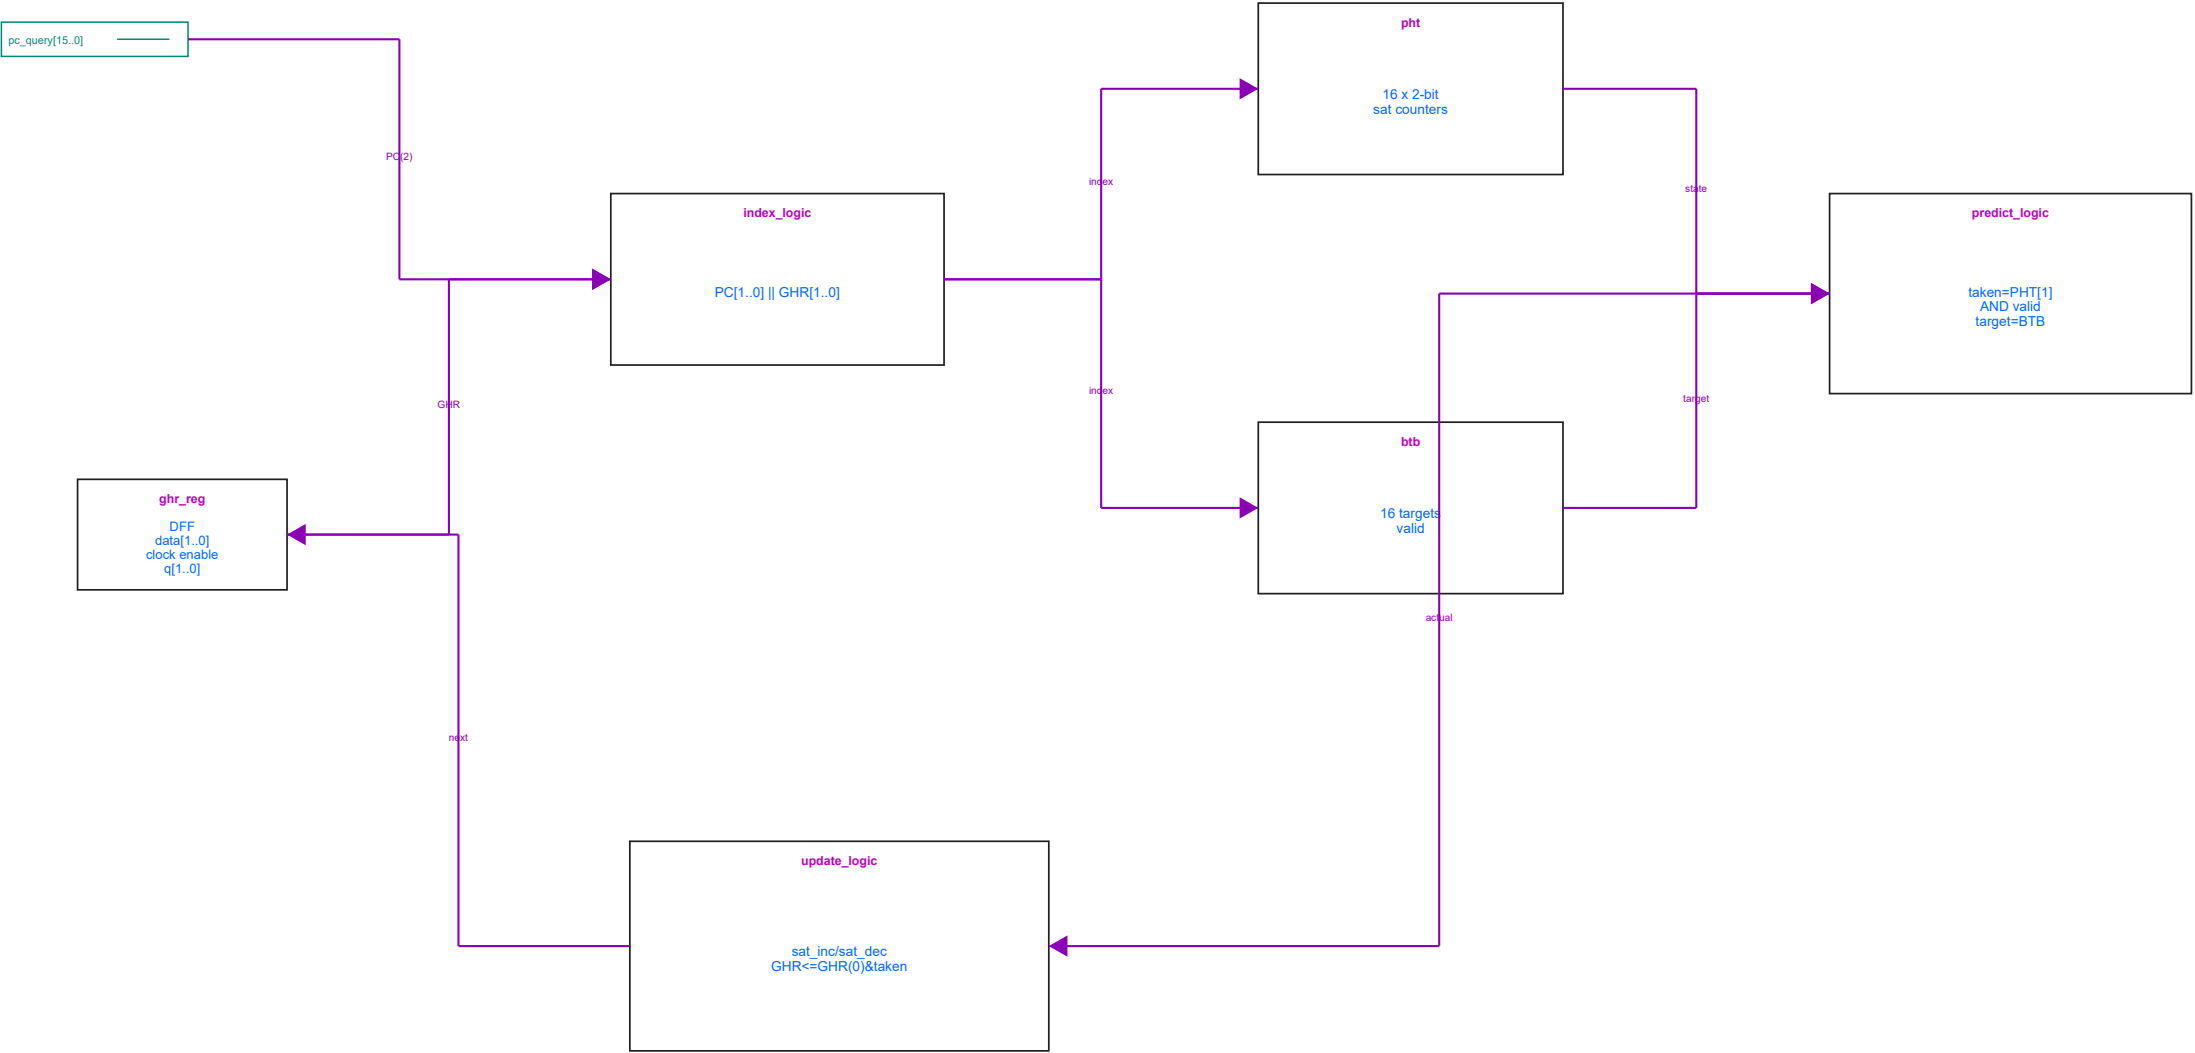

ПРИЛОЖЕНИЕ Щ
Схема блока предсказателя переходов

Разраб. Власов Р.Е.
Пров. Третьяков